
KONDYGNACJA -1: ZL III

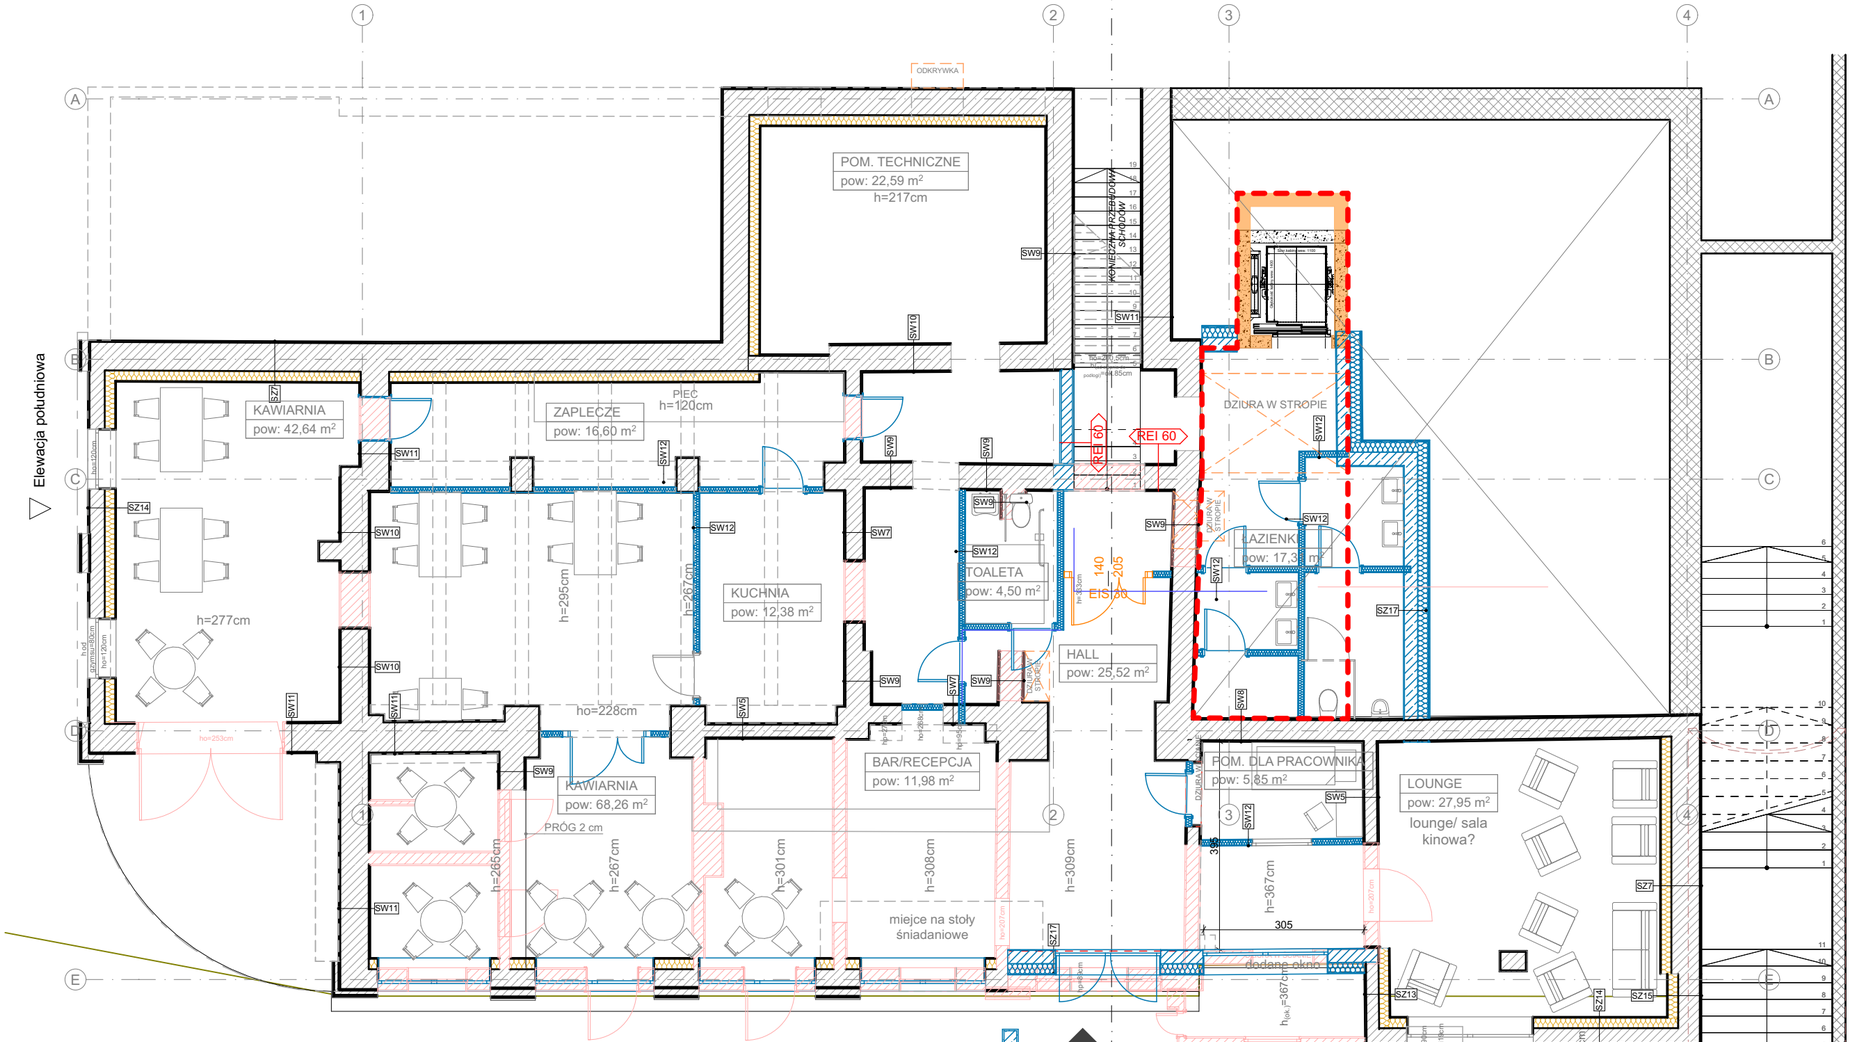

SZ 1 - Ściana zewnetrzna z izolacją wewnętrzną

tynk zewnętrzny	≈ 3 cm
cegła pełna	≈ 34 cm
termoizolacja	20 cm
tynk wewnetrzny	1,5 cm

SZ 2 - Ściana zewnetrzna z izolacją wewnętrzną

tynk zewnętrzny	≈ 3 cm
cegła pełna	≈ 39 cm
termoizolacja	20 cm
tynk wewnetrzny	1,5 cm

SZ 3 - Ściana zewnetrzna z izolacją wewnętrzną

tynk zewnętrzny	1,5 cm
termoizolacja	20 cm
cegła pełna	≈ 39 cm
tynk wewnetrzny	≈ 3 cm

SZ 4 - Ściana zewnetrzna z izolacją wewnętrzną

tynk zewnętrzny	≈ 3 cm
cegła pełna	≈ 44 cm
termoizolacja	20 cm
tynk wewnetrzny	1,5 cm

SZ 5 - Ściana zewnetrzna z izolacją zewnętrzną

tynk zewnętrzny	1,5 cm
termoizolacja	20 cm
cegła pełna	≈ 44 cm
tynk wewnetrzny	≈ 3 cm

SW 1 - Ściana wewnętrzna 7 - 14 cm

tynk wewnetrzny	≈ 2 cm
cegła pełna	-
tynk wewnetrzny	≈ 2 cm

SW 2 - Ściana wewnętrzna 15 - 19 cm

tynk wewnetrzny	≈ 3 cm
cegła pełna	-
tynk wewnetrzny	≈ 3 cm

SW 3 - Ściana wewnętrzna 20 - 24 cm

tynk wewnetrzny	≈ 3 cm
cegła pełna	-
tynk wewnetrzny	≈ 3 cm

SW 4 - Ściana wewnętrzna 25 - 28 cm

tynk wewnetrzny	≈ 3 cm
cegła pełna	-
tynk wewnetrzny	≈ 3 cm

SW 5 - Ściana wewnętrzna 30 - 32 cm

tynk wewnetrzny	≈ 3 cm
cegła pełna	-
tynk wewnetrzny	≈ 3 cm

SW 6 - Ściana wewnętrzna 35 - 38 cm

tynk wewnetrzny	≈ 3 cm
cegła pełna	-
tynk wewnetrzny	≈ 3 cm

SZ 6 - Ściana zewnetrzna z izolacją wewnętrzną

tynk zewnętrzny	≈ 3 cm
cegła pełna	≈ 49 cm
termoizolacja	20 cm
tynk wewnetrzny	1,5 cm

SZ 7 - Ściana zewnetrzna z izolacją wewnętrzną

tynk zewnętrzny	≈ 3 cm
cegła pełna	≈ 54 cm
termoizolacja	20 cm
tynk wewnetrzny	1,5 cm

SZ 8 - Ściana zewnetrzna z izolacją zewnętrzną

tynk zewnętrzny	1,5 cm
termoizolacja	20 cm
cegła pełna	≈ 54 cm
tynk wewnetrzny	≈ 3 cm

SZ 9 - Ściana zewnetrzna z izolacją wewnętrzną

tynk zewnętrzny	≈ 3 cm
cegła pełna	≈ 64 cm
termoizolacja	20 cm
tynk wewnetrzny	1,5 cm

SZ 10 - Ściana zewnetrzna z izolacją zewnętrzną

tynk zewnętrzny	1,5 cm
termoizolacja	20 cm
cegła pełna	≈ 64 cm
tynk wewnetrzny	≈ 3 cm

SW 7 - Ściana wewnętrzna 40 - 44 cm

tynk wewnetrzny	≈ 3 cm
cegła pełna	-
tynk wewnetrzny	≈ 3 cm

SW 8 - Ściana wewnętrzna 45 - 48,5 cm

tynk wewnetrzny	≈ 3 cm
cegła pełna	-
tynk wewnetrzny	≈ 3 cm

SW 9 - Ściana wewnętrzna 50 - 54 cm

tynk wewnetrzny	≈ 3 cm
cegła pełna	-
tynk wewnetrzny	≈ 3 cm

SW 10 - Ściana wewnętrzna 55 - 59 cm

tynk wewnetrzny	≈ 3 cm
cegła pełna	-
tynk wewnetrzny	≈ 3 cm

SW 11 - Ściana wewnętrzna 60 - 63,5 cm

tynk wewnetrzny	≈ 3 cm
cegła pełna	-
tynk wewnetrzny	≈ 3 cm

SW 11 - Ściana wewnętrzna 70 cm

tynk wewnetrzny	≈ 3 cm
cegła pełna	-
tynk wewnetrzny	≈ 3 cm

SZ 11 - Ściana zewnetrzna z izolacją wewnętrzną

folia hydroizolacyjna	-
ściana żelbetowa	25 cm
termoizolacja	20 cm
tynk wewnetrzny	1,5 cm

SZ 12 - Ściana zewnetrzna z izolacją wewnętrzną

tynk zewnętrzny	≈ 3 cm
cegła pełna	≈ 22 cm
termoizolacja	20 cm
tynk wewnetrzny	1,5 cm

SZ 13 - Ściana zewnetrzna z izolacją wewnętrzną

tynk zewnętrzny	≈ 3 cm
cegła pełna	≈ 24 cm
termoizolacja	20 cm
tynk wewnetrzny	1,5 cm

SZ 14 - Ściana zewnetrzna z izolacją wewnętrzną

tynk zewnętrzny	≈ 3 cm
cegła pełna	≈ 29 cm
termoizolacja	20 cm
tynk wewnetrzny	1,5 cm

SZ 15 - Ściana zewnetrzna z izolacją wewnętrzną

tynk zewnętrzny	≈ 3 cm
cegła pełna	≈ 41 cm
termoizolacja	20 cm
tynk wewnetrzny	1,5 cm

SW 12 - Ściana wewnętrzna lekka

2x płyta GK	
wełna mineralna	
2x płyta GK	

P 1 - Strop międzykondygnacyjny

parkiet	
wylewka	2 cm
ziełbet	5 cm
tynk wewnętrzny	33 cm
	≈ 3 cm

P 2 - Strop międzykondygnacyjny

lastriko	3 cm
-	10 cm
wylewka	7 cm
papa	-
wylewka betonowa	10 cm
cegła	12 cm
tynk wewnętrzny	≈ 3 cm

D 1 - Dach

blacha na rąbek	-
taśma wygłuszająca	-
łaty wg wytycznych producenta	-
kontrłaty wg wytycznych producenta	-
membrana paroprzepuszczalna	-
deskowanie pełne	-
konstrukcja dachu-krokwie / wełna mineralna w płytach lub luzem	20cm
stalowy system - rusztwsporczy pod montaz płyty GK z wypełnieniem przestrzeni wełną mineralną	10cm
paroizolacja	-
płyta g-k	1,25 cm
płyta g-k	1,25 cm

SZ 16 - Ściana zewnetrzna z izolacją wewnętrzną

tynk zewnętrzny	≈ 3 cm
cegła pełna	≈ 50 cm
termoizolacja	20 cm
tynk wewnetrzny	1,5 cm

SZ 17 - Ściana zewnetrzna z izolacją zewnętrzną

tynk zewnętrzny	1,5 cm
termoizolacja	20 cm
pustak ceramiczny	25 cm
izolacja przeciwwodna	-
tynk wewnetrzny	1,5 cm

SZ 18 - Ściana zewnetrzna z izolacją zewnętrzną

tynk zewnętrzny	1,5 cm
termoizolacja	20 cm
pustak ceramiczny	18 cm
izolacja przeciwwodna	-
tynk wewnetrzny	1,5 cm

F 1 - Ściana fundamentowa

folia kubełkowa	-
polistyren ekstrudowany (mocowany na kołkach systemowych)	15 cm
izolacja przeciwwilgociowa	-
grubowarstwowa PCI Pecimor 2K	-
warstwa mineralnej zaprawy uszczelniającej PCI Barraseal	-
żelbetowa ściana fundamentowa	25 cm
izolacja przeciwwilgociowa	-
grubwarstwowa PCI Pecimor 2K	

P 3 - Podłoga na gruncie

warstwa wykończeniowa	2 cm
wylewka cementowa	6 cm
izolacja termiczna EPS 100	15 cm
izolacja bitumiczna	-
chudy beton	15 cm
podsypka zagęszczona mechanicznie	15 cm
grunt rodzimy po zdjęciu humusu	- cm

P 4 - Strop międzykondygnacyjny

warstwa wykończeniowa	2 cm
wylewka cementowa	6 cm
styropian akustyczny EPS 100	5 cm
płyta żelbetowa wg projektu	16 cm
techniczngo konstrukcji	
styropian biały Swisspor EPS 70-038	20 cm
fasada	
tynk cementowo - wapienny	1,5 cm

P 5 - Stropodach

2x papa termozgrzewalna	-
izolacja termiczna	4 cm
izolacja termiczna	20 cm
paroizolacja	-
betonowa warstwa spadkowa	4 cm
płyta żelbetowa wg projektu	20 cm
technicznego konstrukcji	
tynk cementowo - wapienny	1,5 cm

LEGENDA

- ściany nośne i działowe - istniejące
- ściany podlegające usunięciu
- **ściany nośne do usunięcia po uzyskaniu zgody uprawnionego konstruktora i zaproponowaniu rozwiązania zamiennego przez niego !!!**
- ściany działowe - lokalizacja wymaga weryfikacji
- ściany nośne - projektowane
- ściany działowe - projektowane - ścianka lekka: 2x płyta GK, wełna mineralna 10 cm, 2x płyta GK
- ściany zewnętrzne - projektowane
- projektowane drzwi
- projektowane drzwi (EI 30, 89, 202)
- drzwi do usunięcia
- termoizolacja - projektowana, gr. 20 cm
- długość dojść ewakuacyjnych
- lokalizacja do weryfikacji

UWAGI:

1. *Wszystkie wymiary należy sprawdzić na budowie*
2. *Elementy konstrukcji wg projektu konstrukcji*
3. *Przed zamówieniem stolarki, wymiary otworów należy sprawdzić na budowie*
4. *Przed wylaniem stropu należy zamontować dobrane wpusty lub przygotować miejsce pod ich montaż zgodnie z wytycznymi producenta*
5. *Umiejscowienie przebić instalacyjnych należy odczytać z rysunków branży sanitarnej*
6. *Rysunek należy rozpatrywać łącznie z rysunkami branżowymi*
7. *W celu zapewnienia swobodnego przepływu powietrza między pomieszczeniami należy zastosować drzwi z podcięciami*

nazwa inwestycji

Przebudowa, rozbudowa i nadbudowa budynków mieszkalnego i gospodarczego oraz zmiana sposobu użytkowania na budynek hotelowo-usługowy wraz z niezbędną infrastrukturą

adres inwestycji	ul. Kulczyńskiego 8, 38-440 Iwonicz-Zdrój obręb: 0001 Iwonicz-Zdrój nr działki: 1313 gmina: Iwonicz-Zdrój powiat: krośnieński
identyfikator działki ewid.	180703_4.0001.1313
inwestor	Capital Towers Sp. z o.o. SK-A ul. Piłsudskiego 34, 35-001 Rzeszów
ARCHITEKTURA	
projektant	mgr inż. arch. Aleksandra Słowik upr. nr:18/PKOKK/2021
zespół projektowy	mgr inż. arch. Magdalena Mazurkiewicz
	mgr inż. arch. Maria Konopka
	mgr inż. arch. Wiktoria Bielska
	inż. arch. Magdalena Obszyńska

CoZa STUDIO

nr rysunku	A-01	Rzut poziomu 0
skala		
data	12.2024	

CoZa Studio, Plac Kilińskiego 6, 35-005 Rzeszów, kom. 608 393 184